
VUE EN PLAN — AMÉNAGEMENT

Échelle 1:24 (1/2 po = 1 pi) si imprimé à 100 %, format lettre

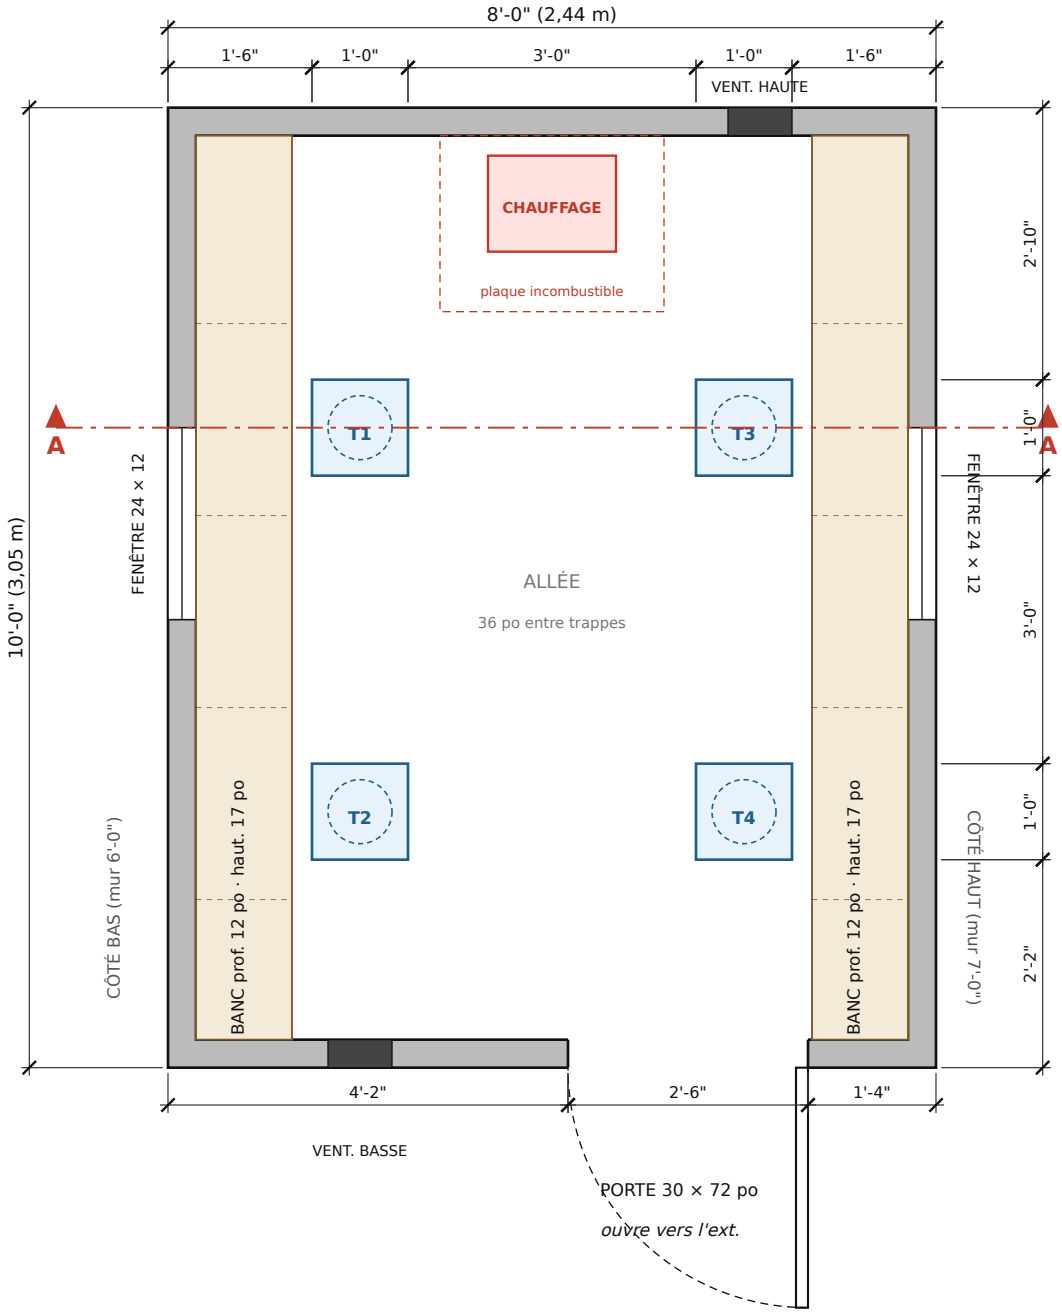

NOTES

1. Dimensions hors-tout 8'-0" × 10'-0" (2,44 × 3,05 m). Largeur sous 8'-6" : transportable sur remorque sans permis spécial.
2. Plancher à 13 1/2 po au-dessus de la glace (patins 2×8 + solives 2×6 + CP 3/4).
3. 4 trappes T1 à T4 de 12 × 12 po, logées entre les solives. Couvercles affleurants en CP 3/4 avec poignée encastrée. Trou à la tarière de 8 à 10 po sous chaque trappe.
4. Bancs de 12 po de profondeur et 17 po de hauteur sur toute la longueur, couvercles à charnières pour le rangement.
5. Porte 30 × 72 po qui ouvre vers l'extérieur (libère l'intérieur). Loquet intérieur et cadenas extérieur.
6. Toit à une pente : mur gauche 6'-0", mur droit 7'-0" (pente 1 1/2 : 12).
7. Chauffage au propane homologué pour l'intérieur, posé sur une plaque incombustible. Respecter les dégagements du fabricant.
8. Ventilation basse (porte) et haute (arrière) toujours ouvertes, détecteur de monoxyde de carbone (CO) à piles et extincteur ABC obligatoires.
9. Afficher nom, adresse et téléphone du propriétaire à l'extérieur ; vérifier le règlement municipal (dates de pose et de retrait sur le lac).

Cotes en pieds-pouces. Vérifier toutes les cotes au chantier.

PROJET	FEUILLE	DATE	STATUT	NO
Cabane à pêche blanche 8 × 10 pi sur patins	**Vue en plan — aménagement**	**2026-11-07**	**Préliminaire**	**1 / 4**


ÉLÉVATION AVANT (porte)

Échelle 1:32 (3/8 po = 1 pi)



ÉLÉVATION LATÉRALE DROITE (côté haut)

Échelle 1:32 (3/8 po = 1 pi)

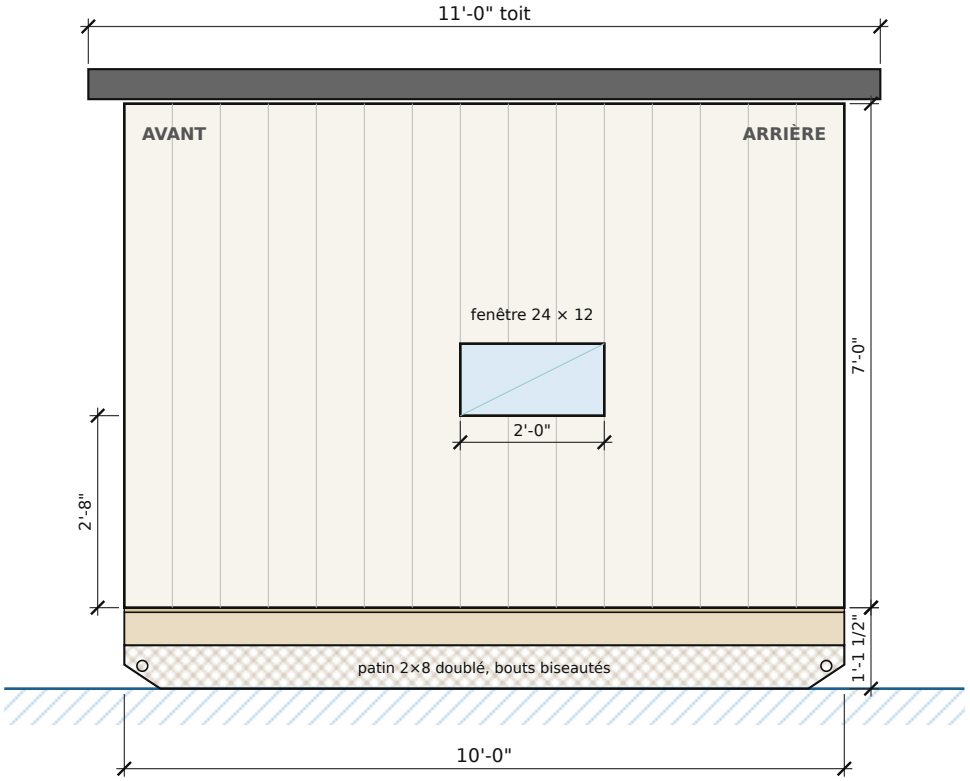


FINITION

1. Revêtement extérieur : tôle d'acier prépeinte calibre 29 posée à la verticale sur OSB 7/16 (ou contreplaqué peint). Couleur foncée = gain solaire.
2. Côté gauche : identique en miroir, mur de 6'-0". Arrière : sans ouverture, ventilation haute sous le toit.

PROJET	FEUILLE	DATE	STATUT	NO
Cabane à pêche blanche 8 × 10 pi sur patins	**Élévations avant et latérale**	**2026-11-07**	**Préliminaire**	**2 / 4**

OSSATURE DU PLANCHER (vue de dessus)

Échelle 1:24 — contreplaqué retiré

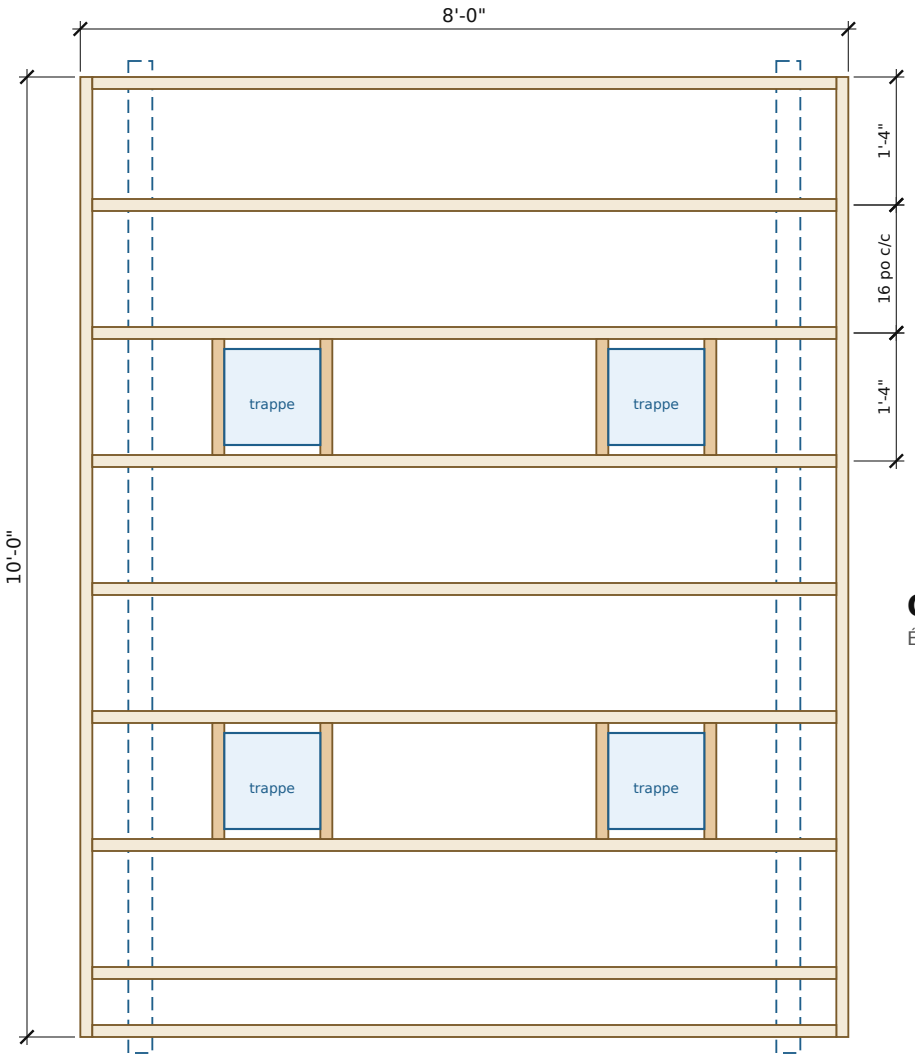


Patins (pointillés bleus) : 2×8 traité doublé, 10'-0", à 6 po des rives.

Chevêtres 2×6 de chaque côté des trappes. Attaches anti-soulèvement solive/patin.

Plancher : CP 3/4 traité, collé et vissé ; découper les 4 trappes après la pose.


OSSATURE MUR LATÉRAL DROIT (côté haut)

Échelle 1:32 — 2×3 @ 16 po c/c, vue de l'intérieur

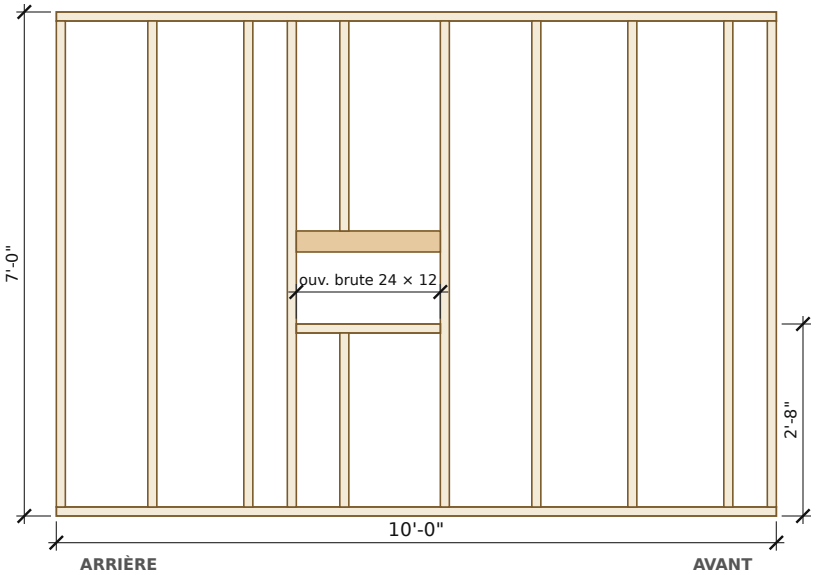

OSSATURE MUR AVANT (porte)

Échelle 1:32 — posé entre les murs latéraux, vue de l'extérieur

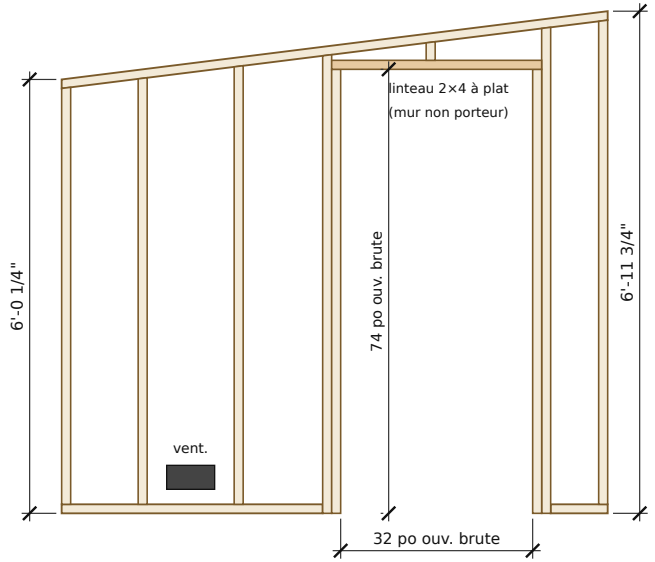


Mur arrière : même gabarit, sans porte, ventilation haute. Chevrons 2×4 vis-à-vis des montants.

PROJET	FEUILLE	DATE	STATUT	NO
Cabane à pêche blanche 8 × 10 pi sur patins	**Ossature plancher et murs**	**2026-11-07**	**Préliminaire**	**3 / 4**

COUPE A-A (vers l'arrière)

Échelle 1:24 (1/2 po = 1 pi)

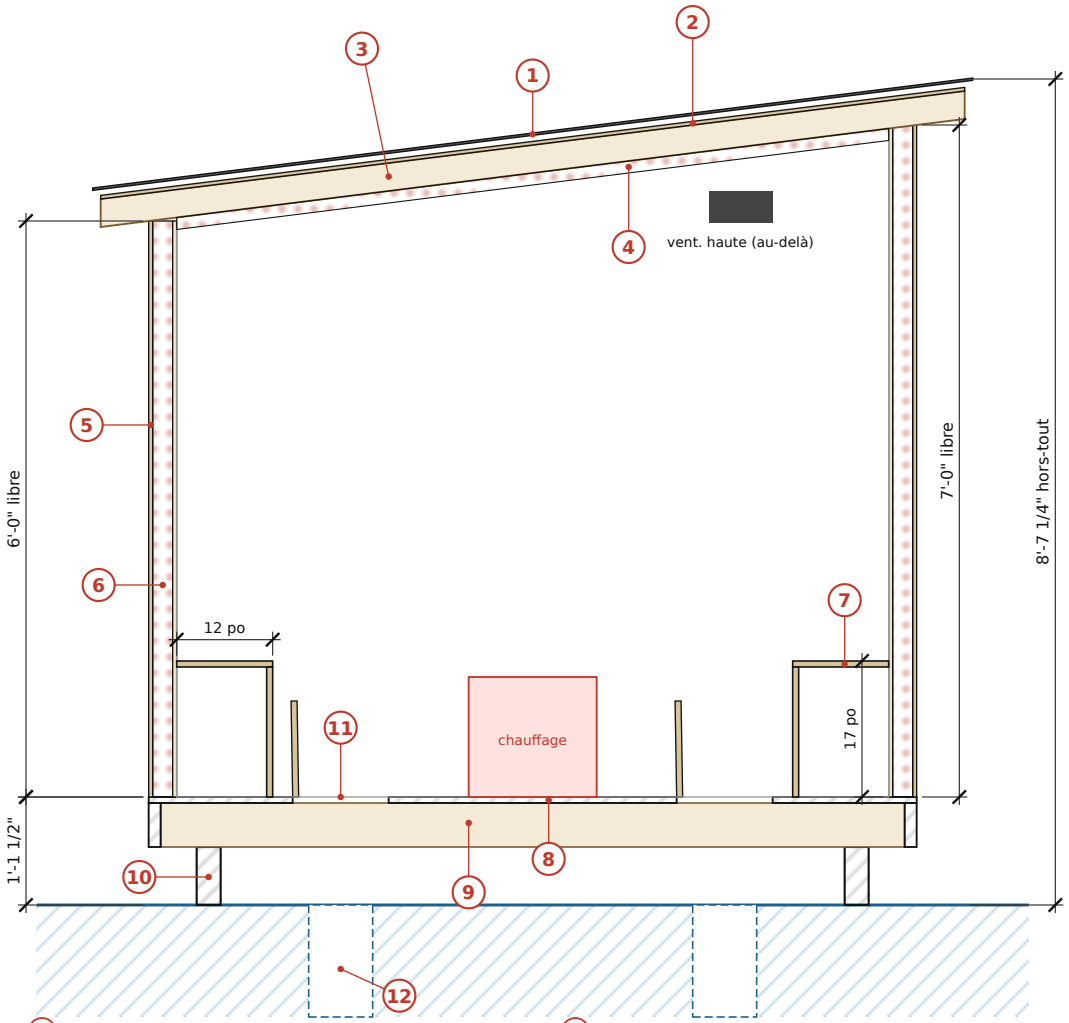

1. Tôle prépeinte cal. 29 sur fourrures 1×3
2. Pontage OSB 7/16 po
3. Chevrons 2×4 @ 24 po c/c, débord 6 po
4. Isolant XPS 1 1/2 po entre chevrons
5. Tôle + OSB 7/16 po (revêtement)
6. Montants 2×3 @ 16 po + XPS + CP 1/4
7. Banc : dessus CP 3/4, couvercle à charnières
8. Plancher CP 3/4 po traité, collé-vissé
9. Solives 2×6 traité @ 16 po c/c
10. Patin 2×8 traité doublé (coupé)
11. Trappe 12 × 12 ouverte
12. Trou dans la glace, tarière 8 à 10 po

LISTE DE MATÉRIAUX (estimation)

Ajouter 10 % de perte. Bois traité pour tout ce qui touche la glace.

BASE	
Patins	4 × 2×8 × 10 pi traité
Solives de rive	2 × 2×6 × 10 pi traité
Solives + chevêtres	11 × 2×6 × 8 pi traité
Plancher	3 × CP 3/4 po 4×8 traité
MURS	
Montants, lisses, sablières	≈ 48 × 2×3 × 8 pi
Linteaux	2 × 2×4 × 8 pi
Revêtement	8 × OSB 7/16 po 4×8
Tôle murs	≈ 230 pi² (cal. 29)
TOIT	
Chevrons @ 24 po	6 × 2×4 × 10 pi
Fourrures	8 × 1×3 × 12 pi
Pontage	4 × OSB 7/16 po 4×8
Tôle toit	4 × 3 pi × 9 pi + moulures
ISOLATION / INTÉRIEUR	
Isolant XPS 1 1/2 po	≈ 19 panneaux 2×8 pi
Finition intérieure (murs + plafond)	9 × CP 1/4 po 4×8
Bancs + couvercles trappes	3 × CP 3/4 po 4×8 + 6 × 2×3
OUVERTURES	
Porte 30 × 72 maison	3 pentures, loquet, moraillon
Fenêtres	2 × polycarbonate 1/4 po 24×12
Ventilation	2 grilles réglables 4×10 po
QUINCAILLERIE	
Vis 3 po ext., vis 1 5/8 po	≈ 5 lb + 3 lb
Vis à tôle à rondelle	≈ 300
Attaches anti-soulèvement	18 (solive/patin, chevron/mur)
Œillets de remorquage	2 × tire-fond à œil 1/2 po
SÉCURITÉ	
Détecteur CO, extincteur ABC	1 + 1
Plaque incombustible	1 × panneau ciment 1/2 po

PROJET	FEUILLE	DATE	STATUT	NO
Cabane à pêche blanche 8 × 10 pi sur patins	**Coupe A-A et matériaux**	**2026-11-07**	**Préliminaire**	**4 / 4**