
VUE EN PLAN — AMÉNAGEMENT


Échelle 1:24 (1/2 po = 1 pi) · avant (timon) à gauche

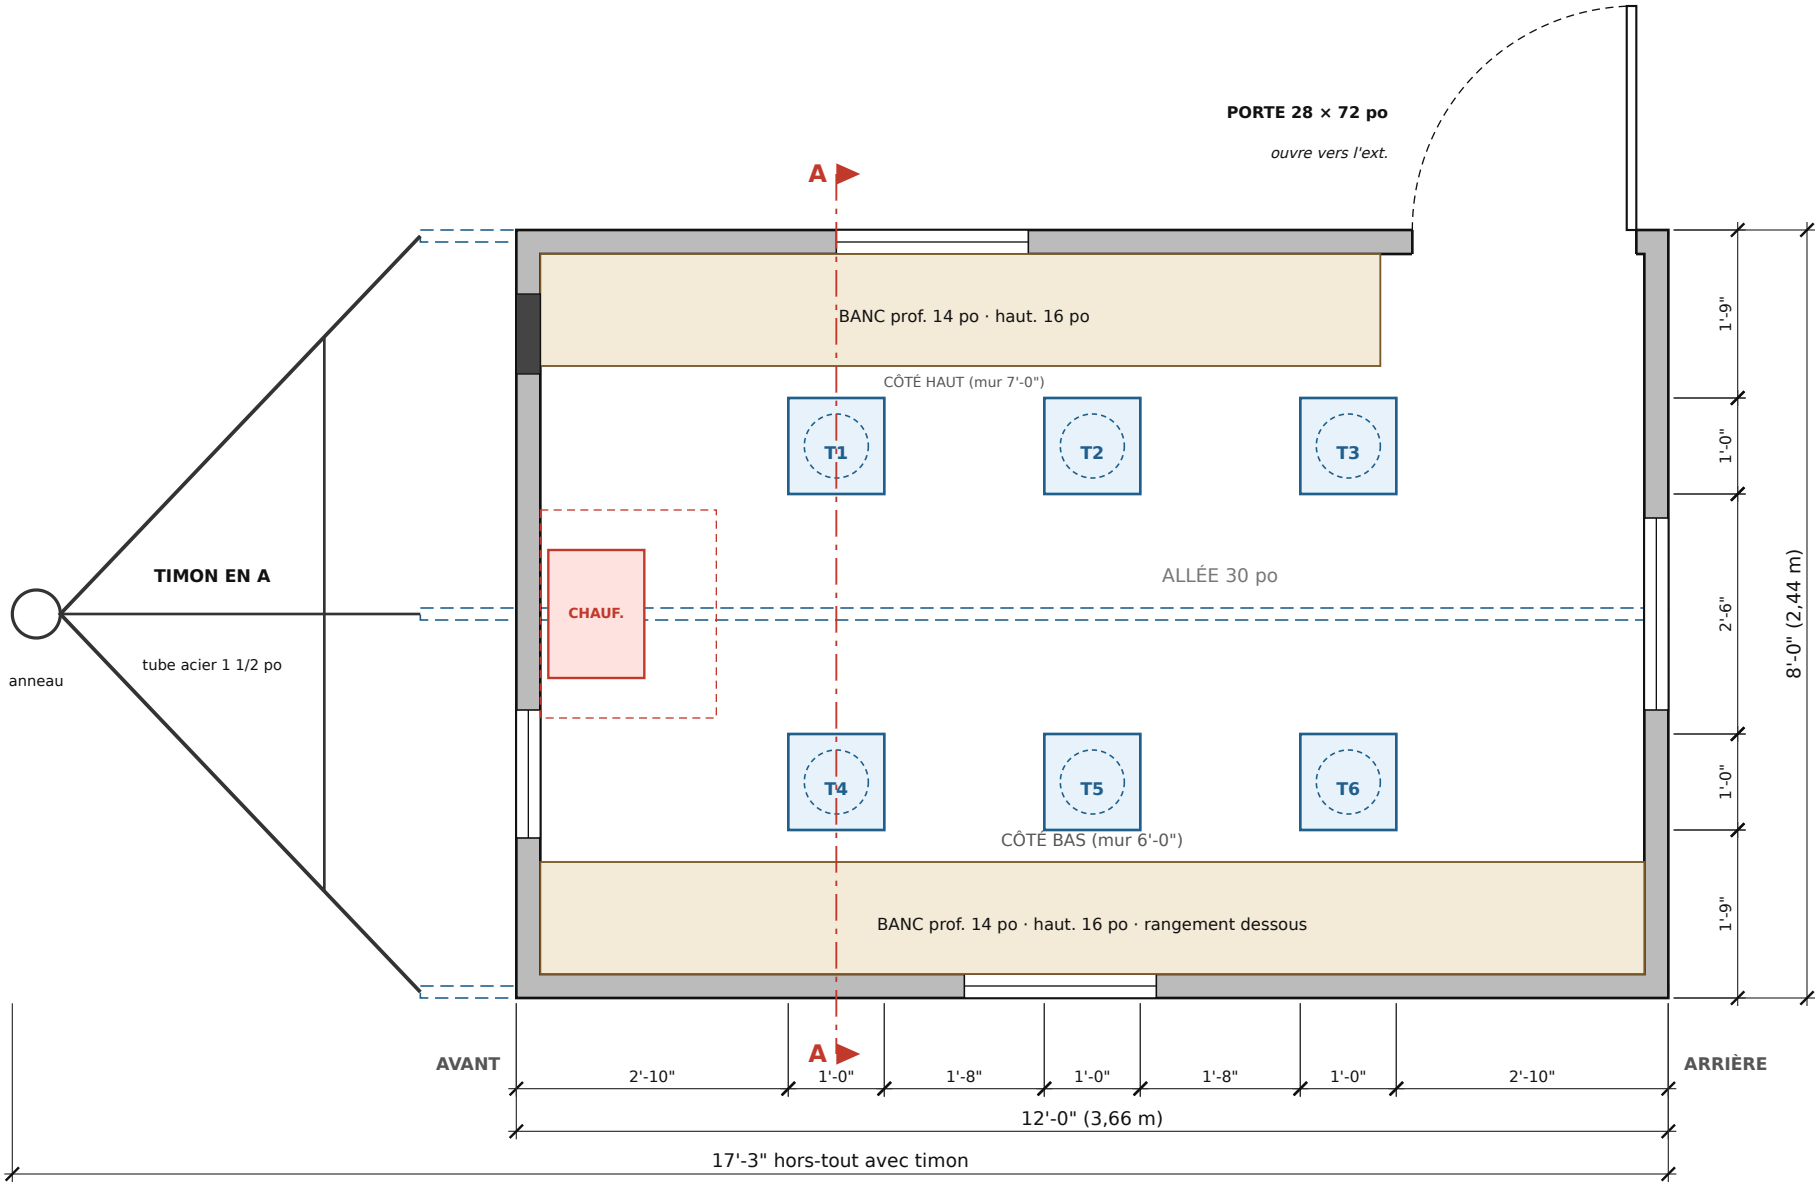

PROJET	FEUILLE	DATE	STATUT	NO
Cabane à pêche 8 × 12 pi monopente — motoneige	**Vue en plan — aménagement**	**2026-11-08**	**Préliminaire**	**1 / 6**

ÉLÉVATION CÔTÉ HAUT (porte)

Échelle 1:24 (1/2 po = 1 pi) · vue de l'extérieur, avant à droite

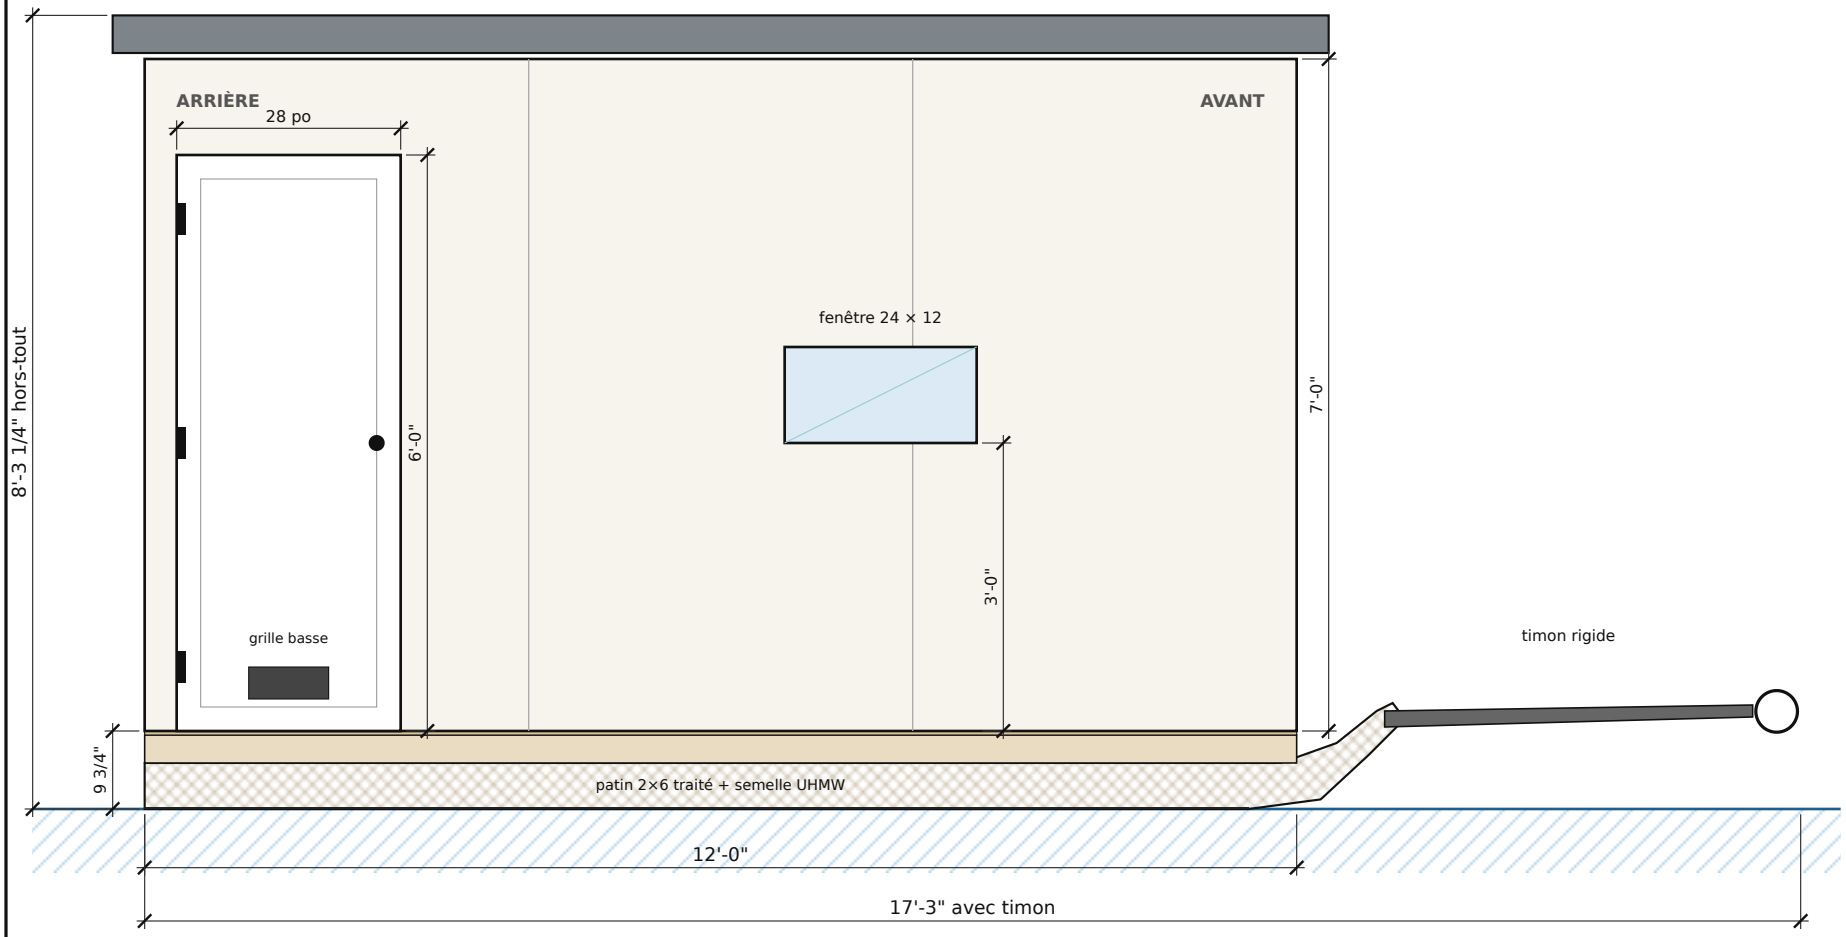


TOIT MONOPENTE 1 1/2:12

1. Le toit descend du côté haut (7'-0") vers le côté bas (6'-0") : 1 1/2 po par pied sur 8 pi, soit 12 po d'écart. La neige et l'eau partent du côté bas, loin de la porte. Pente faible : poser la tôle avec ruban scellant aux recouvrements et vérifier la pente minimale du fabricant.
2. Chevrons 2×4 @ 24 po qui portent d'un mur à l'autre (pas de faîte), débord de 6 po aux deux égouts et de 4 po aux bouts.

PROJET	FEUILLE	DATE	STATUT	NO
Cabane à pêche 8 × 12 pi monopente — motoneige	**Élévation côté haut**	**2026-11-08**	**Préliminaire**	**2 / 6**


ÉLÉVATION AVANT (timon)

Échelle 1:24 (1/2 po = 1 pi)

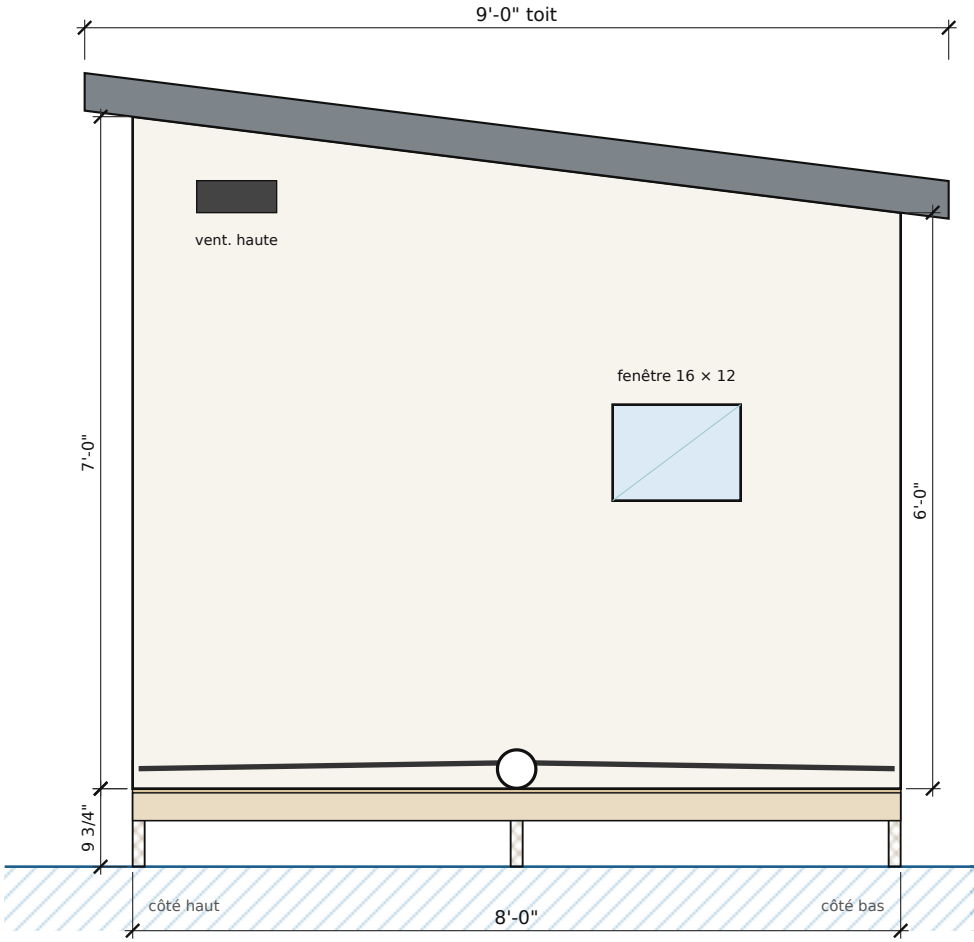

ÉLÉVATION ARRIÈRE

Échelle 1:24 (1/2 po = 1 pi)

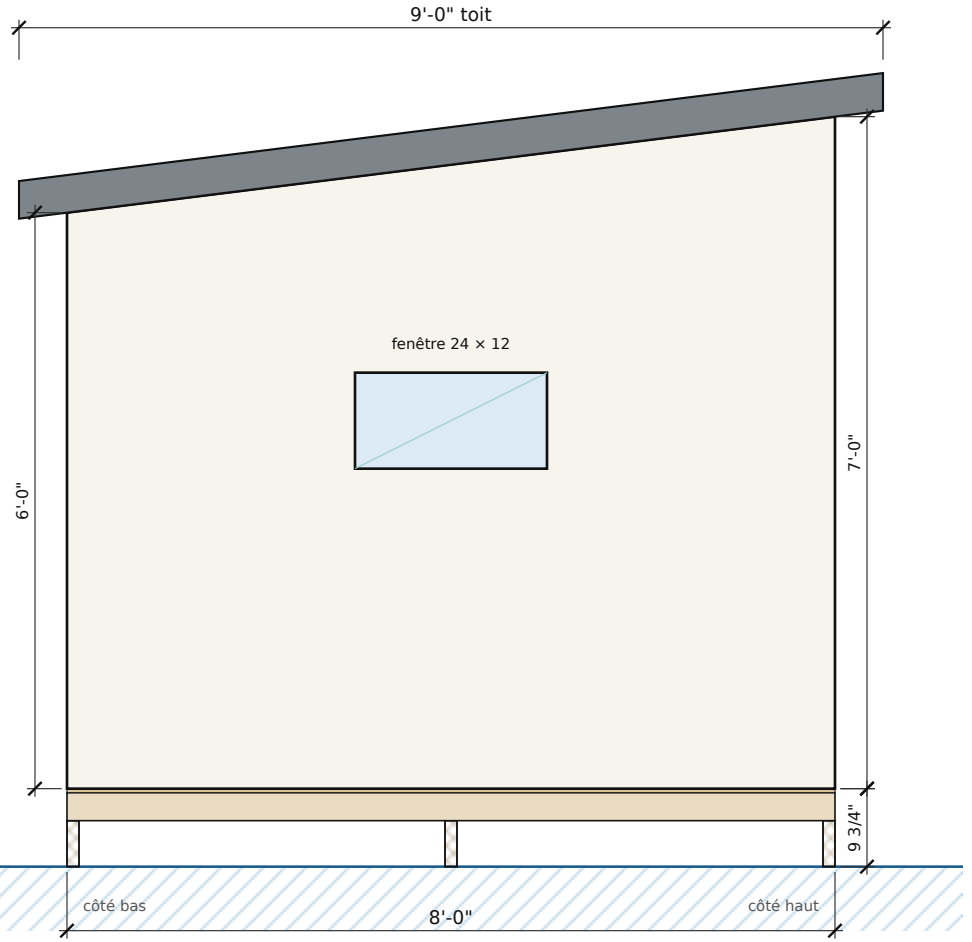

ABOUTS


1. Les murs avant et arrière suivent la pente du toit : 7'-0" du côté haut, 6'-0" du côté bas. Hauteur hors-tout 8'-3 1/4".

2. Avant : fenêtre 16 × 12 du côté bas, ventilation haute du côté haut, timon en A. Arrière : fenêtre 24 × 12 centrée.

PROJET	FEUILLE	DATE	STATUT	NO
Cabane à pêche 8 × 12 pi monopente — motoneige	**Élévations avant et arrière**	**2026-11-08**	**Préliminaire**	**3 / 6**

COUPE A-A (vers l'arrière)

Échelle 1:24 (1/2 po = 1 pi)

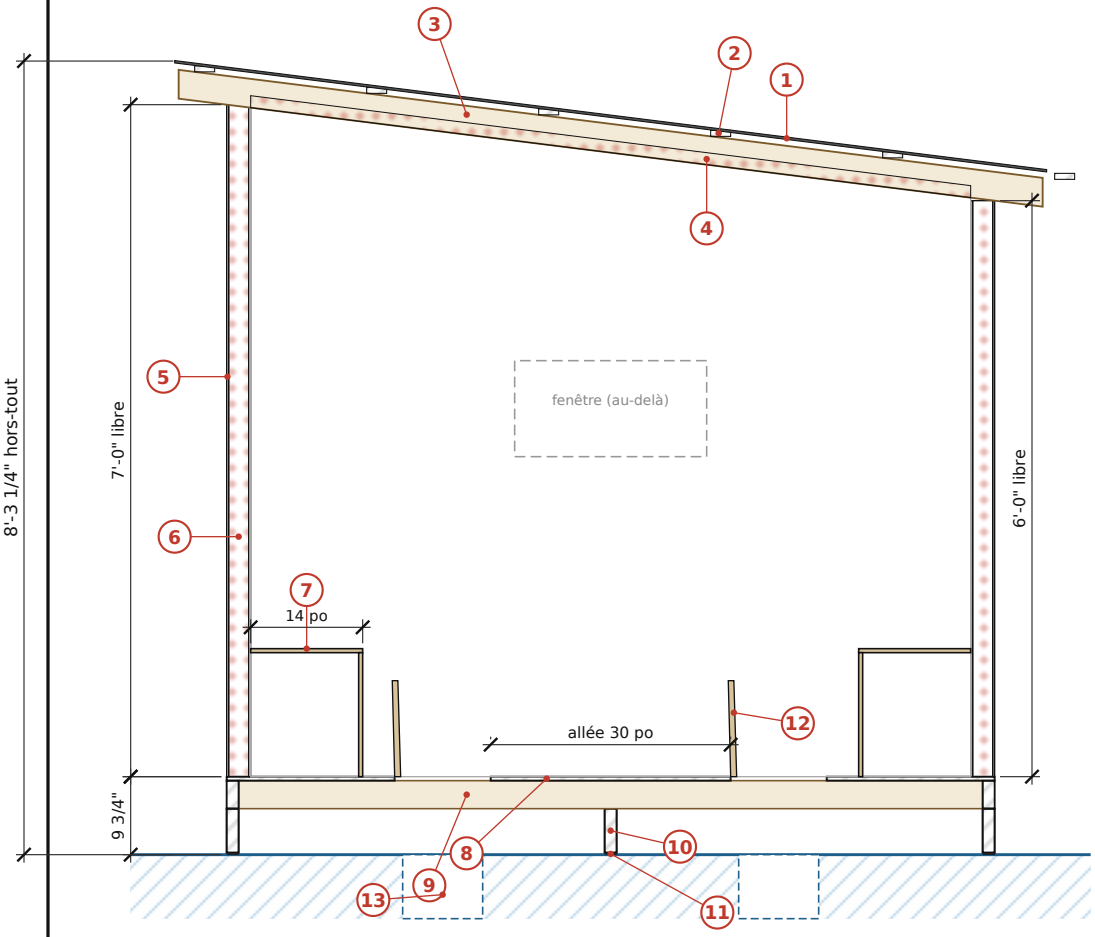

LÉGENDE

1. Tôle prépeinte cal. 29 (ou aluminium)
2. Fourrures 1×3 @ 24 po
3. Chevrons 2×4 @ 24 po c/c, pente 1 1/2:12
4. Isolant XPS 1 1/2 po entre chevrons
5. Revêtement CP 1/4 extérieur, peint
6. Montants 2×3 @ 24 po + XPS + panneau 1/4
7. Bancs : dessus et devant CP 1/2
8. Plancher CP 1/2 traité, collé-vissé
9. Traverses 2×4 @ 16 po (portée 4 pi)
10. 3 patins 2×6 traité sur chant (coupés)
11. Semelles de glisse UHMW 1/4 po
12. Trappe 12 × 12 ouverte (6 en tout)
13. Trou dans la glace, tarière 8 à 10 po


POURQUOI 3 PATINS

1. À 8 pi de large, un patin central coupe la portée des traverses en deux (4 pi) : des 2×4 suffisent au lieu de 2×8, et le plancher ne fléchit pas en sentier.

PROJET	FEUILLE	DATE	STATUT	NO
Cabane à pêche 8 × 12 pi monopente — motoneige	**Coupe A-A**	**2026-11-08**	**Préliminaire**	**4 / 6**

CADRE DE PLANCHER, PATINS ET TIMON (vue de dessus)

Échelle 1:32 — contreplaqué retiré

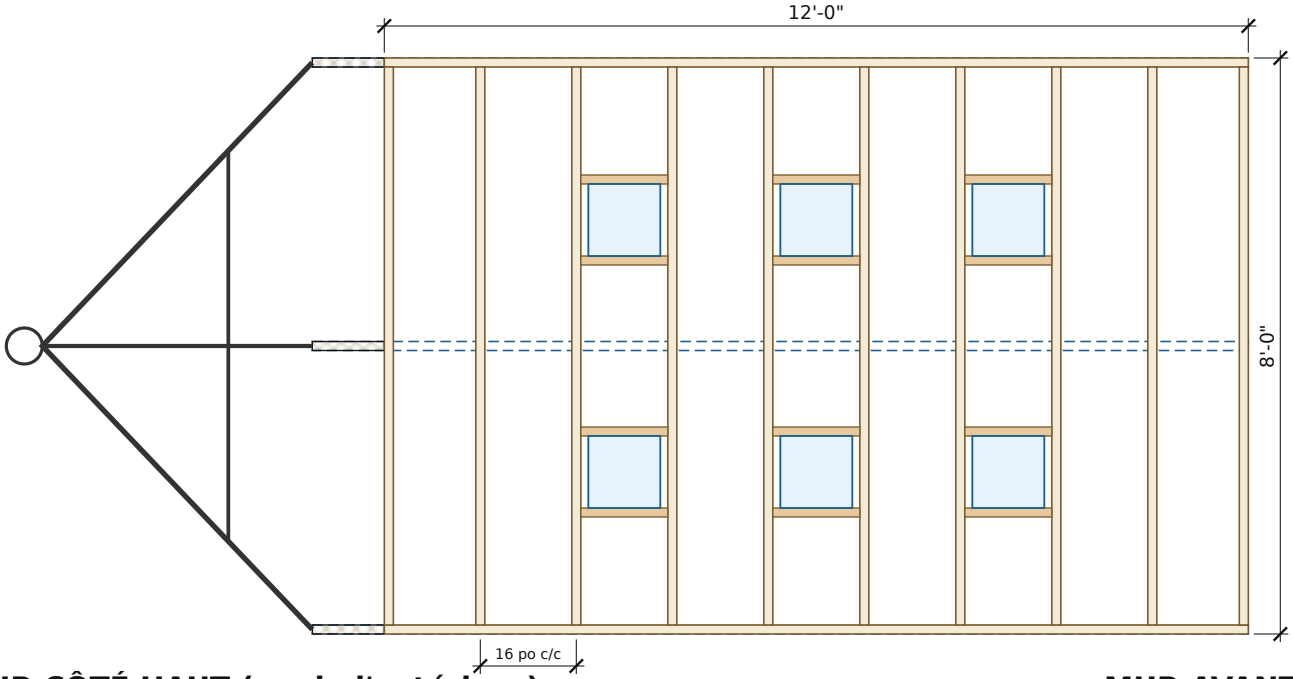


CADRE

1. 2×4 traité sur chant : rives de 12 pi, traverses @ 16 po.
2. Chevêtres 2×4 autour des 6 trappes.
3. 3 patins : sous chaque rive et au centre. Tire-fonds 3/8 × 5 à chaque traverse.
4. Timon : 2 bras + bras central vers l'anneau, traverse de raidissement, boulonné dans le nez des 3 patins.


MUR CÔTÉ HAUT (vu de l'extérieur)

Échelle 1:32 — 2×3 @ 24 po c/c, avant à droite

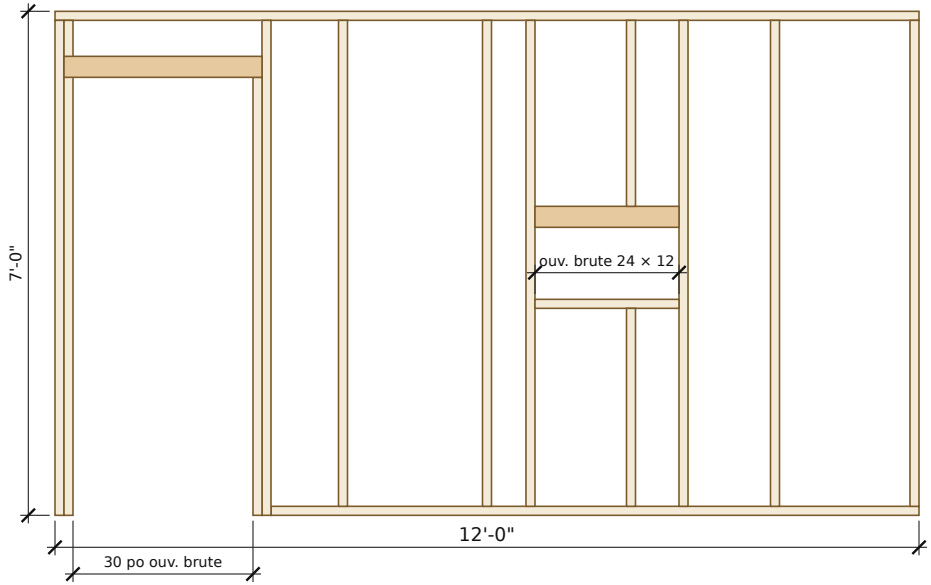

MUR AVANT (vu de l'extérieur)

Échelle 1:32 — entre les murs côtés

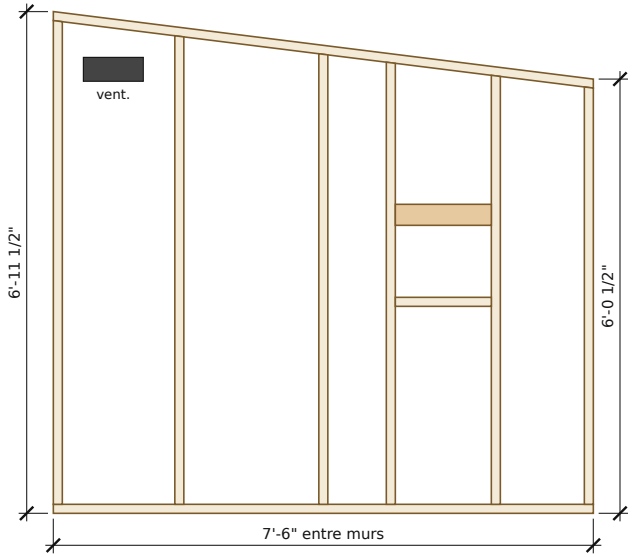

PROJET	FEUILLE	DATE	STATUT	NO
Cabane à pêche 8 × 12 pi monopente — motoneige	**Ossature**	**2026-11-08**	**Préliminaire**	**5 / 6**


LISTE DE MATÉRIAUX (estimation)

Ajouter 10 % de perte. Bois traité pour tout ce qui touche la neige.

BASE, PATINS, TIMON	
Patins (3)	3 × 2×6 × 14 pi traité
Semelles de glisse	3 × UHMW 1/4 × 1 1/2 po × 13 pi
Cadre : rives	2 × 2×4 × 12 pi traité
Cadre : traverses + chevêtres	12 × 2×4 × 8 pi traité
Plancher	3 × CP 1/2 po 4×8 traité
Timon en A	16 pi tube acier 1 1/2 po + anneau + chaîne
MURS	
Montants, lisses, sablières	≈ 37 × 2×3 × 8 pi
Linteaux (porte, fenêtres)	3 × 2×4 × 8 pi
Revêtement extérieur	9 × CP 1/4 po 4×8
Panneau intérieur (option)	7 × CP 1/4 ou panneau 1/8
TOIT	
Chevrons @ 24 po	7 × 2×4 × 10 pi
Fourrures	6 × 1×3 × 14 pi
Tôle	5 × 3 pi × 9'-6" + moulures + ruban scellant
ISOLATION, INTÉRIEUR	
Isolant XPS 1 1/2 po	≈ 22 panneaux 2×8 pi
2 bancs + 6 couvercles	2 × CP 1/2 4×8 + 6 × 2×2 × 8
Plaque incombustible	panneau ciment 1/2 po 2×3 pi
OUVERTURES	
Porte 28 × 72 maison	3 pentures, loquet, moraillon
Fenêtres polycarbonate 1/4	3 × 24×12 + 1 × 16×12
Grilles de ventilation	2 × 4 × 10 po réglables
QUINCAILLERIE, SÉCURITÉ	
Vis ext. 3 et 1 1/4 po	≈ 6 lb + 3 lb
Tire-fonds 3/8 × 5 + boulons timon	30 + 6
Vis à tôle à rondelle	≈ 200
Détecteur CO, extincteur ABC	1 + 1

POIDS ESTIMÉ

Calcul approximatif, à confirmer à la pesée.

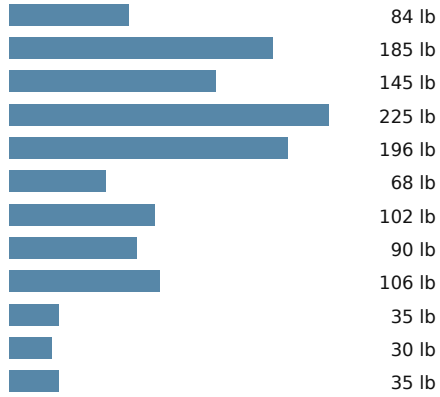

TOTAL TEL QUE DESSINÉ **≈ 1301 lb (590 kg)**

POUR ALLÉGER (≈ 1 100 lb / 500 kg)

1. Tôle d'aluminium au toit : environ 50 lb de moins.
2. Cadre de plancher non traité, peint : environ 40 lb de moins.
3. Pas de panneau intérieur ; bancs en CP 3/8 : environ 35 lb de moins.
4. Revêtement en panneau d'aluminium : environ 60 lb de moins.

À SAVOIR

1. À ce poids, prévoir une motoneige utilitaire ou rouler lentement sur une trace tapée. Vérifier la capacité de remorquage de ta motoneige.
2. Chauffage propane homologué intérieur, ventilation haute et basse, détecteur de CO et extincteur obligatoires.
3. Afficher nom, adresse et téléphone ; vérifier le règlement municipal.